


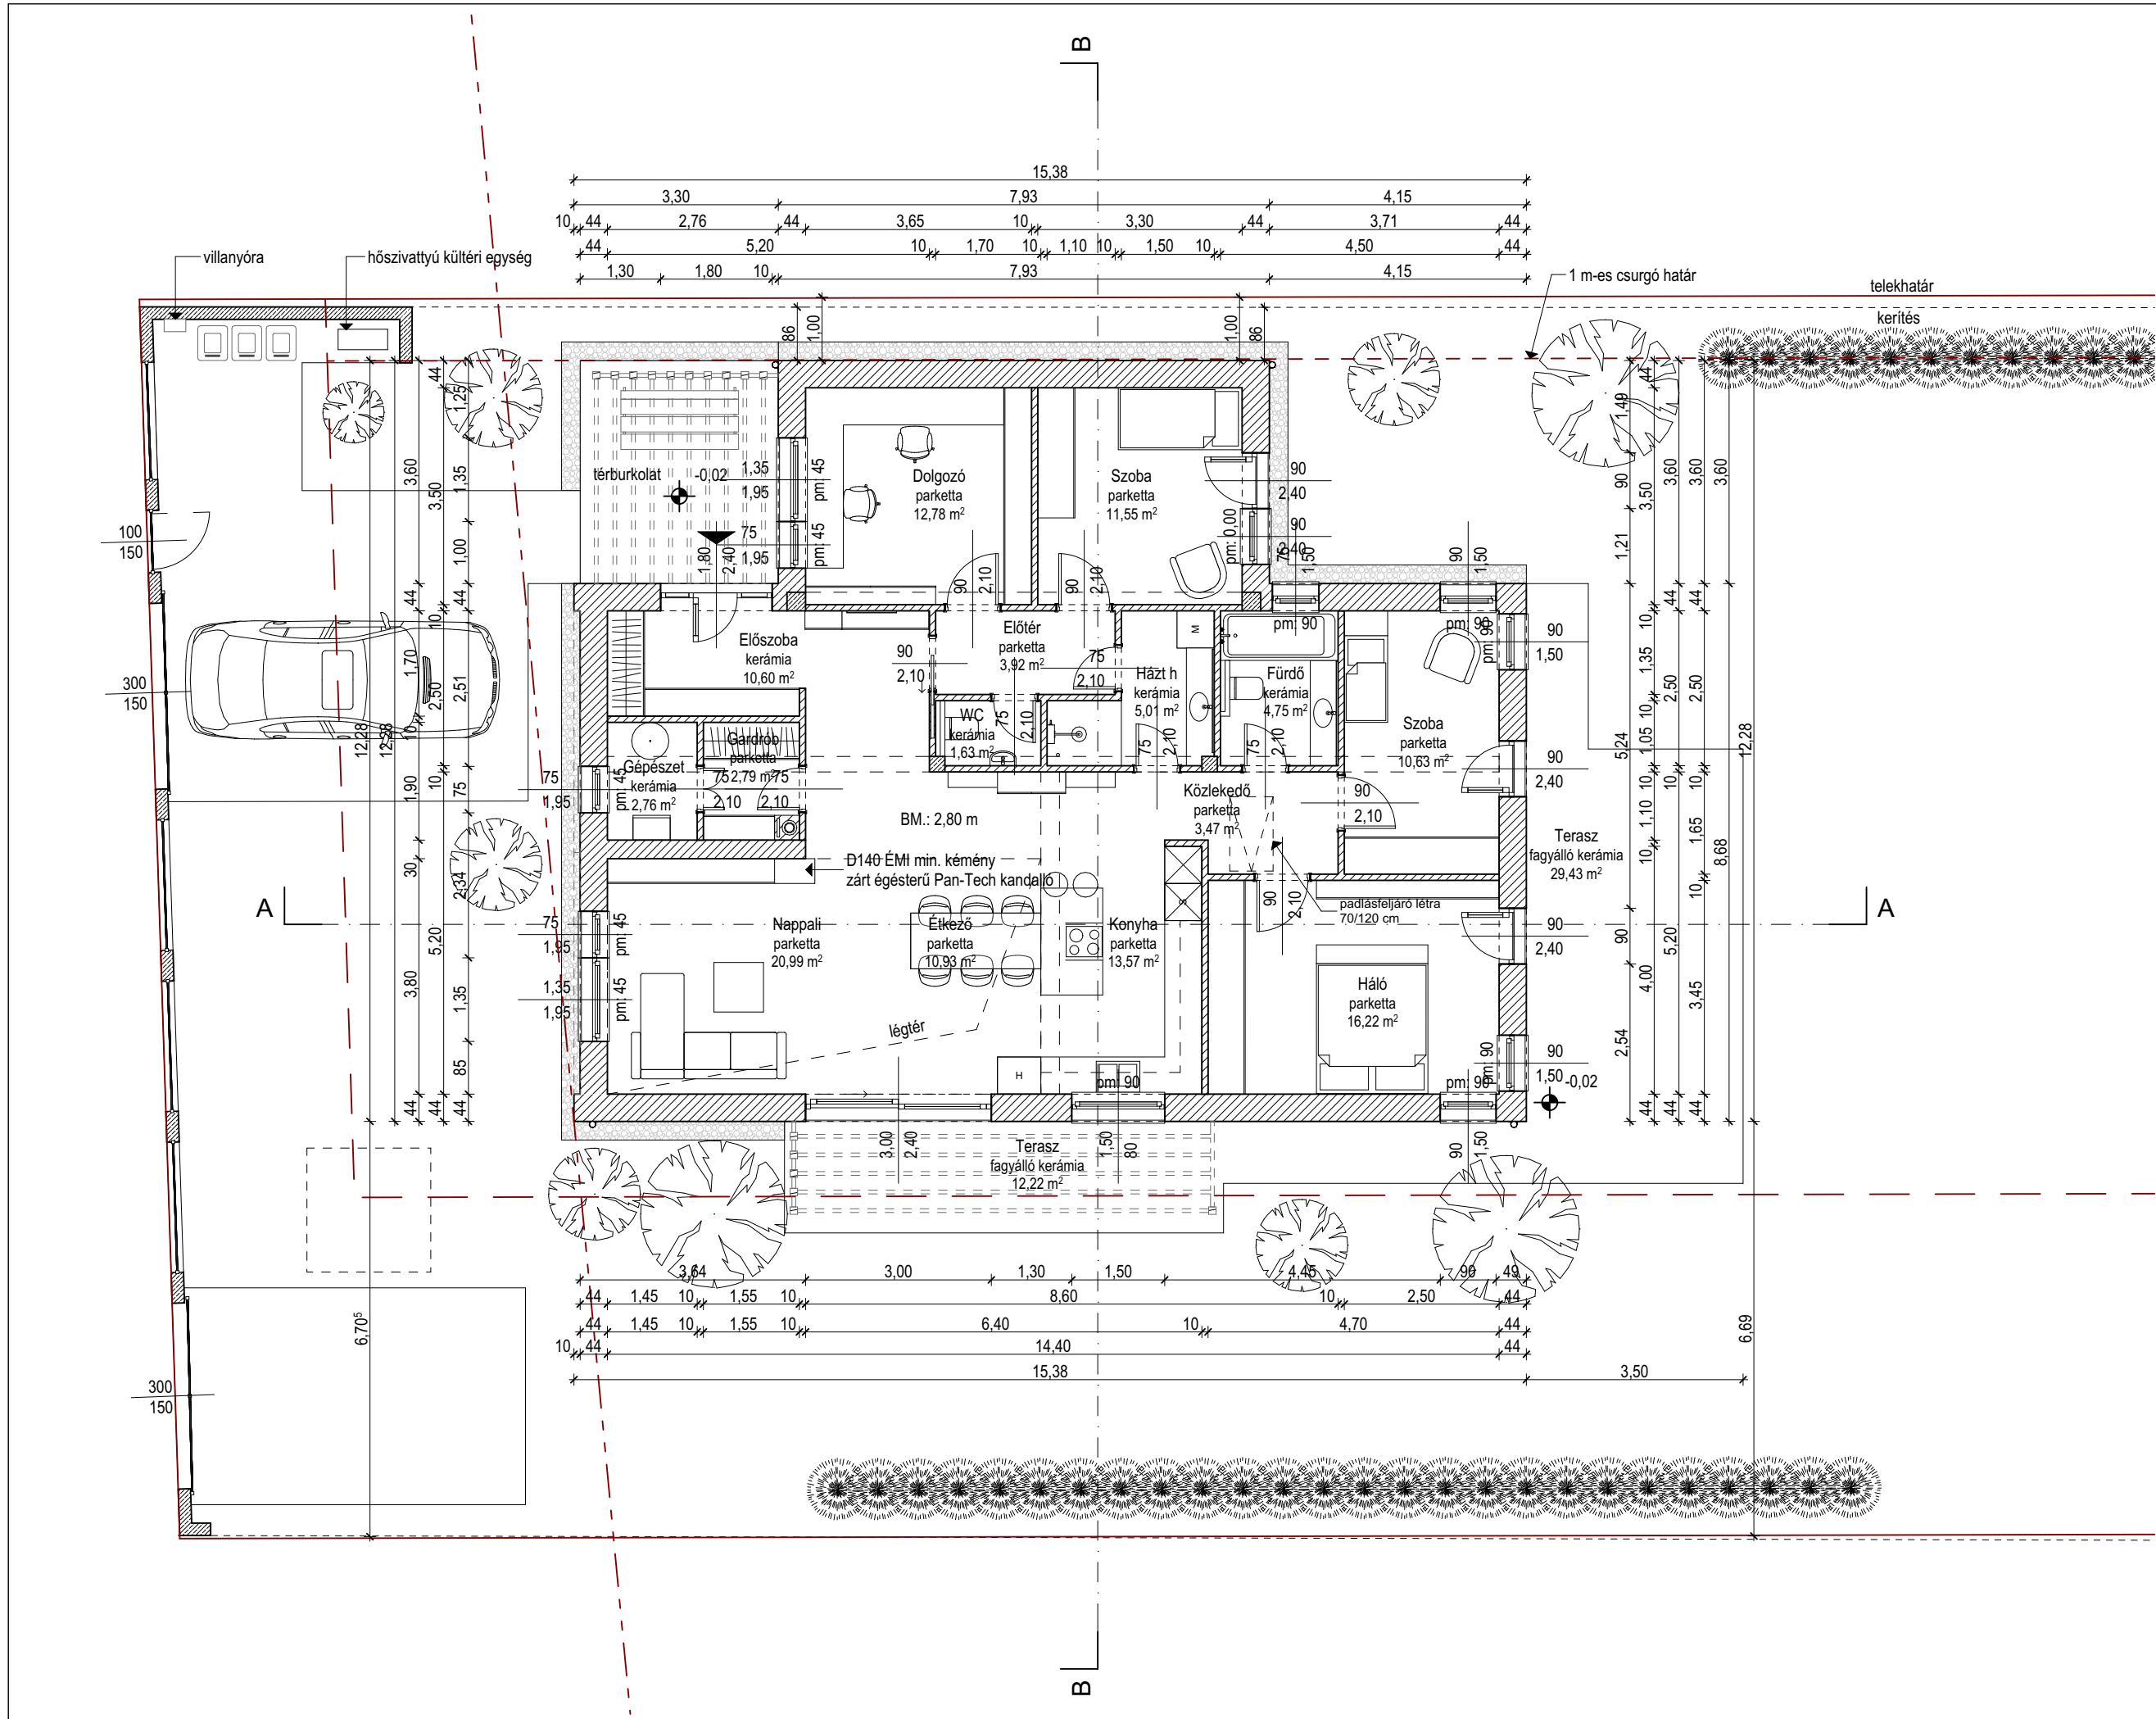

É

K

D

NY

Jelmagyarázat

Vasbeton tartószerkezet - monolit

Fa tartószerkezet

Acél - tartószerkezet

Falazat tartószerkezet - vázkerámia

Válaszfal- vázkerámia

Hőszigetelés - EPS

Hőszigetelés - XPS

Bitumenes vízszigetelés

Esztrich

Zúzott kő

Talaj

MUNKA MEGNEVEZÉSE:

ÚJ EGYLAKÁSOS LAKÓÉPÜLET ÉPÍTÉSE

ÉPÍTÉS HELYE:

2080 Pilisjászfalu
Búzavirág utca 49.
Hrsz.: 1014

ÉPÍTETŐ:

Séf Dániel
1039 Budapest
Nefelejcs utca 8.

ÉPÍTÉSZ TERVEZŐK:

Kiss Gabriella É2 01-1652
Baucad Építésziroda Kft.
H-1164 Budapest, Bányász u. 3. fsz. 1.
Tel.: 30/278-1471
email: baucadepitesziroda@gmail.com

TERVFAJTA:

BEJELENTÉSI TERV

RAJZ MEGNEVEZÉSE:

Földszinti alaprajz

DÁTUM:

2025. 08. 14.

LÉPTÉK:

1:100

E-01 M1